

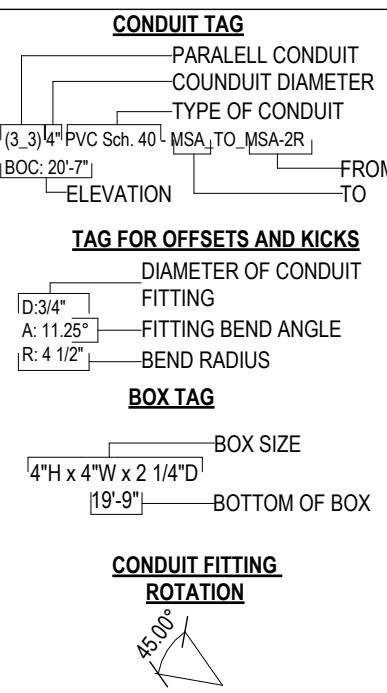
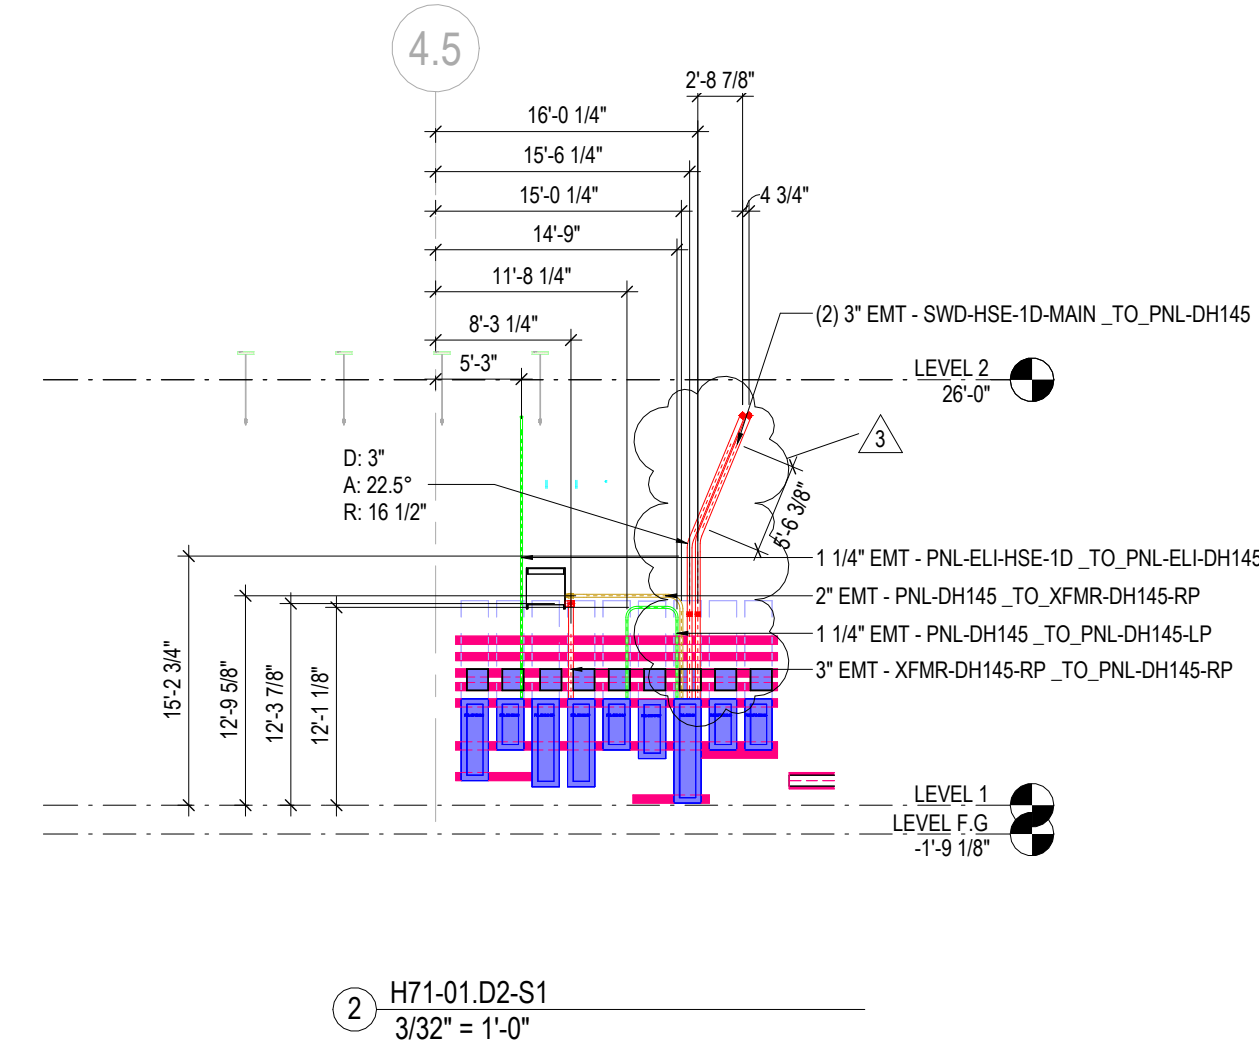


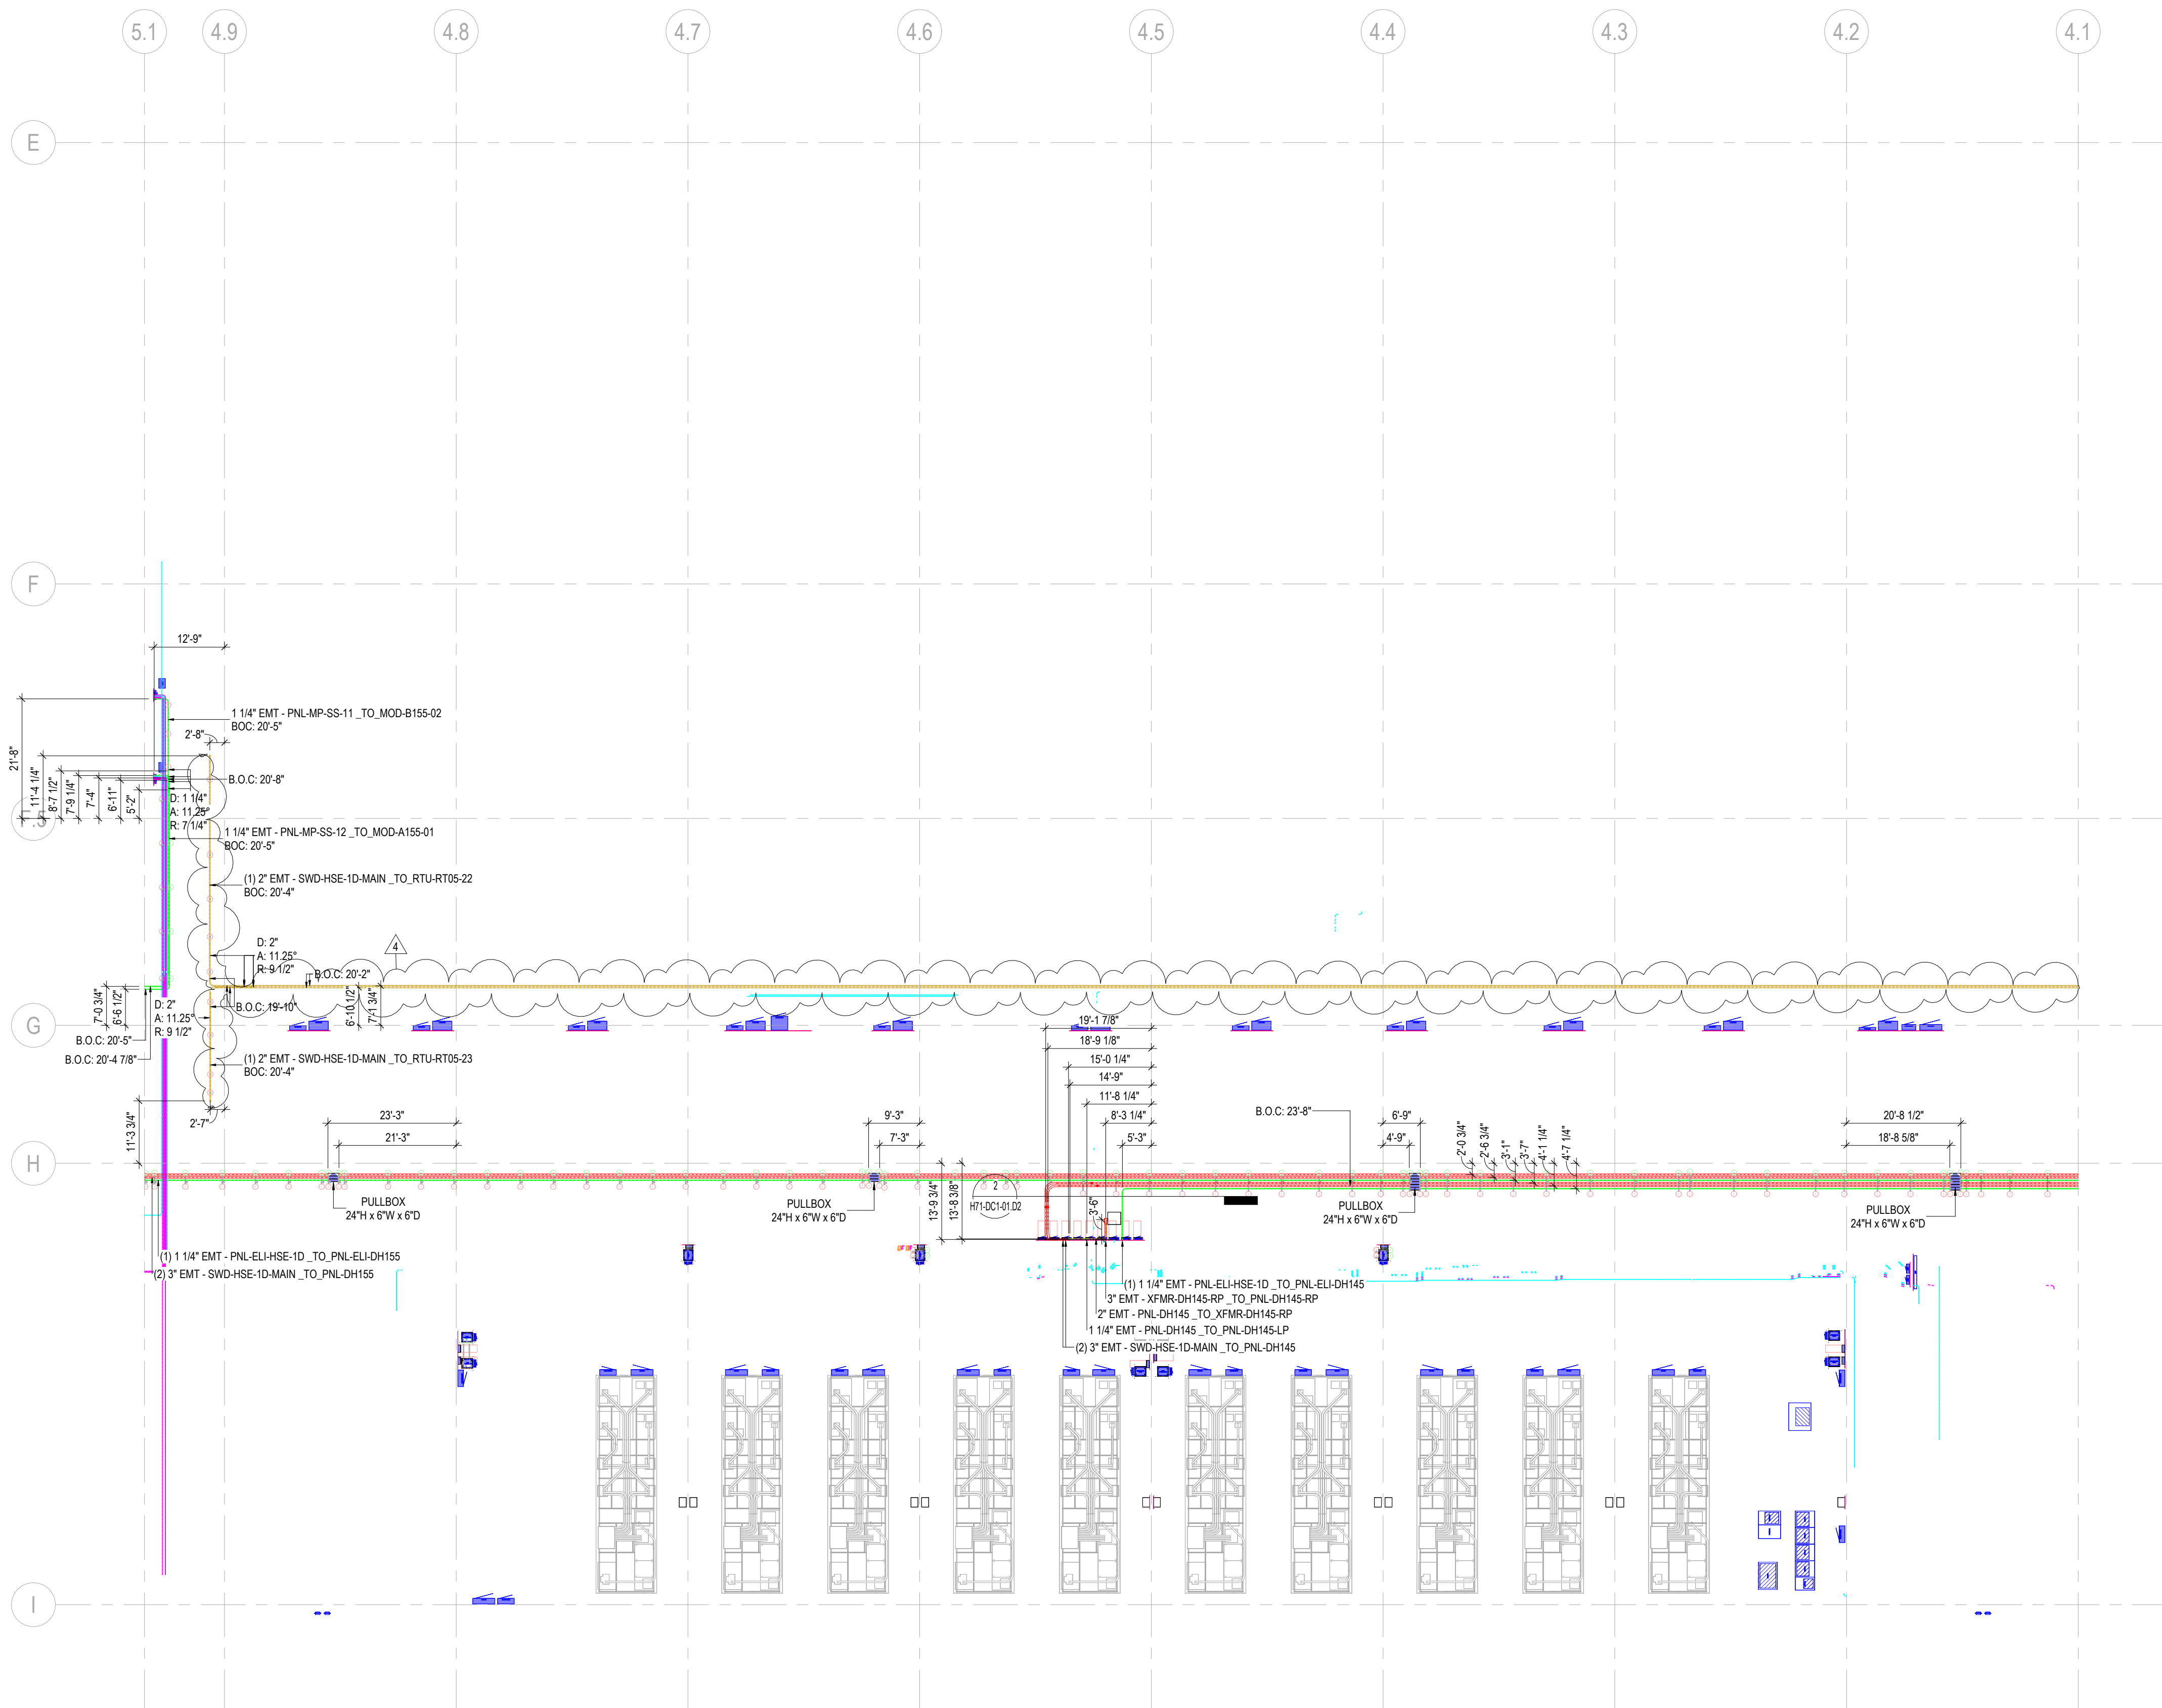

SHEET NOTES
ABBREVIATIONS LEGEND

1/B.O.T. BOTTOM OF TRAY
2/B.O.C. BOTTOM OF CONDUIT
3/T.O.C. TOP OF CONDUIT
4/B.O.B. BOTTOM OF BOX
4/D. DIAMETER
5/R. RADIUS
6/R. RADIUS

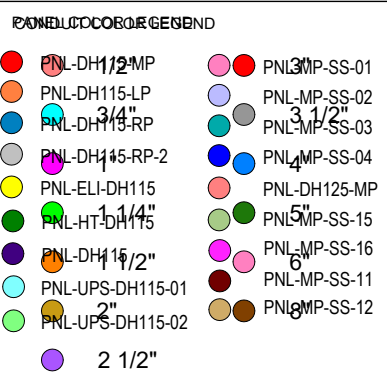

KEY PLAN

F4	E4	D4	C4	B4	A4
F3	E3	D3	C3	B3	A3
F2	E2	D2	C2	B2	A2
F1	E1	D1	C1	B1	A1

REVISIONS

NO.	DATE	DESCRIPTION
1	10/01/2015	REVISED PER REF. #452
2	10/01/2015	REVISED PER REF. #452
3	10/01/2015	REVISED PER REF. #452
4	10/01/2015	REVISED PER REF. #452

PROJECT NAME
QTS-CDR1-DC1

NUMBER
342502

DRWN
AM

CHSR
EL

ISSUE DATE
11/17/25

SCALE
As indicated

SHEET TITLE
**OVERHEAD
DISTRIBUTION -
LEVEL 1 AREA D2**

SHEET NUMBER
H71-DC1-01.D2

7/10/2020 7:14:48 p.m.